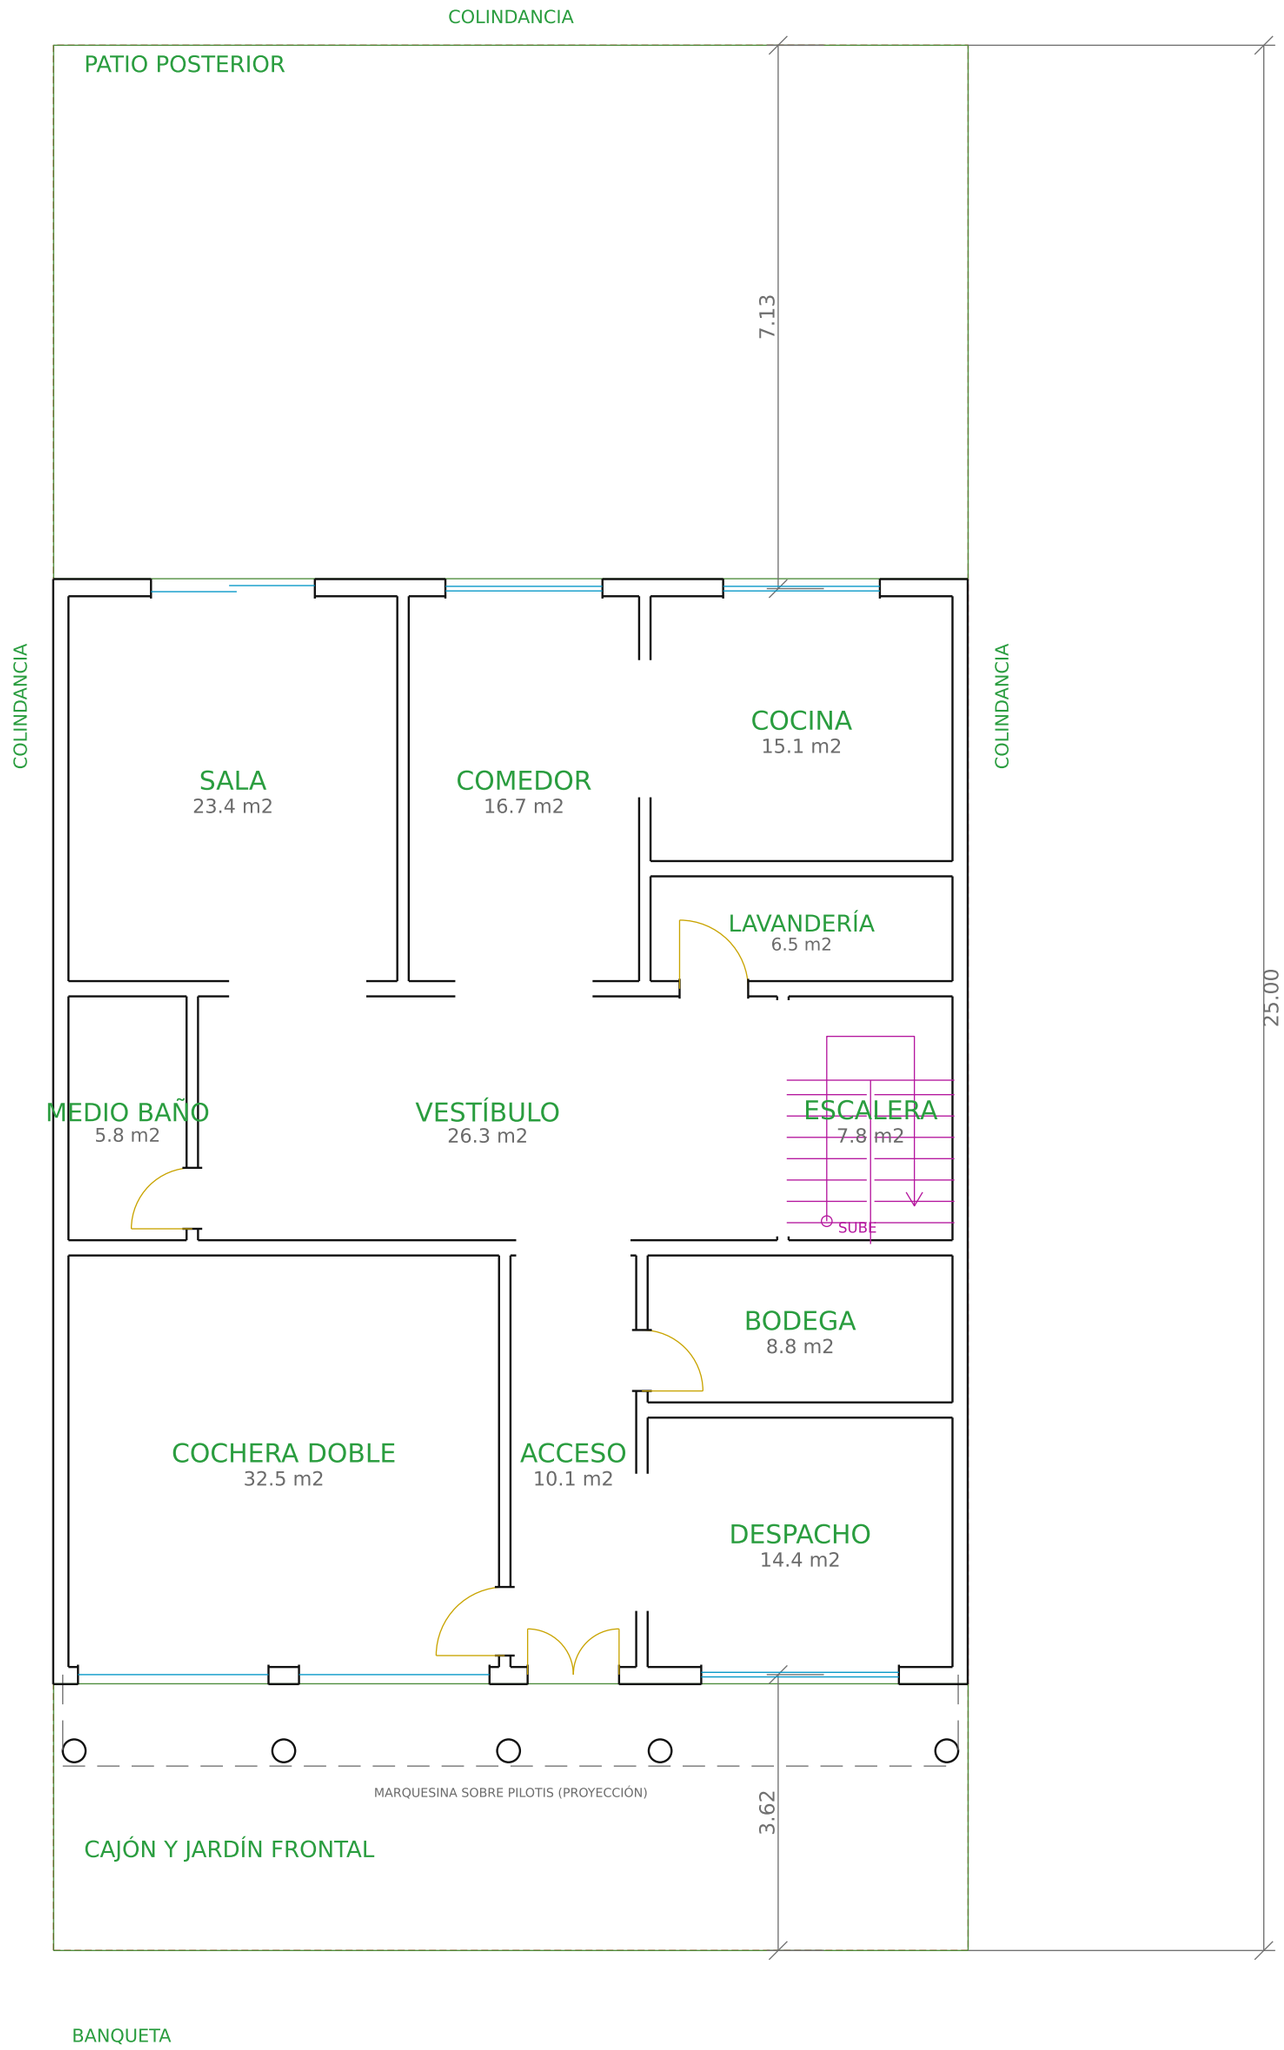

CUADRO DE ÁREAS

Terreno	300.00 m2
Desplante	167.44 m2
C.O.S.	0.56
Construcción total	334.88 m2
C.U.S.	1.12
Área libre	132.56 m2
Área verde (aprox.)	84.00 m2
Niveles	2
Cajones de estacionamiento	2

N

Cotas en metros. Verificar en sitio.
Anteproyecto: el proyecto ejecutivo (estructura, instalaciones, presupuesto y programa) se entrega por separado.
Normativa: Reglamento de Edificaciones de Tijuana y NTC-2017.

VÉRTICE Ingeniería, Arquitectura y Proyectos

CASA PILOTIS

AP-01 Planta de conjunto

Clave: 2026-11-07-casa-moderna-bauhaus Fecha: 2026-11-07 Unidades: metros
Anteproyecto generado automáticamente — sin validez para construcción
Para revisión de: Ing. Miguel Estrada (DRO / Perito en edificación)

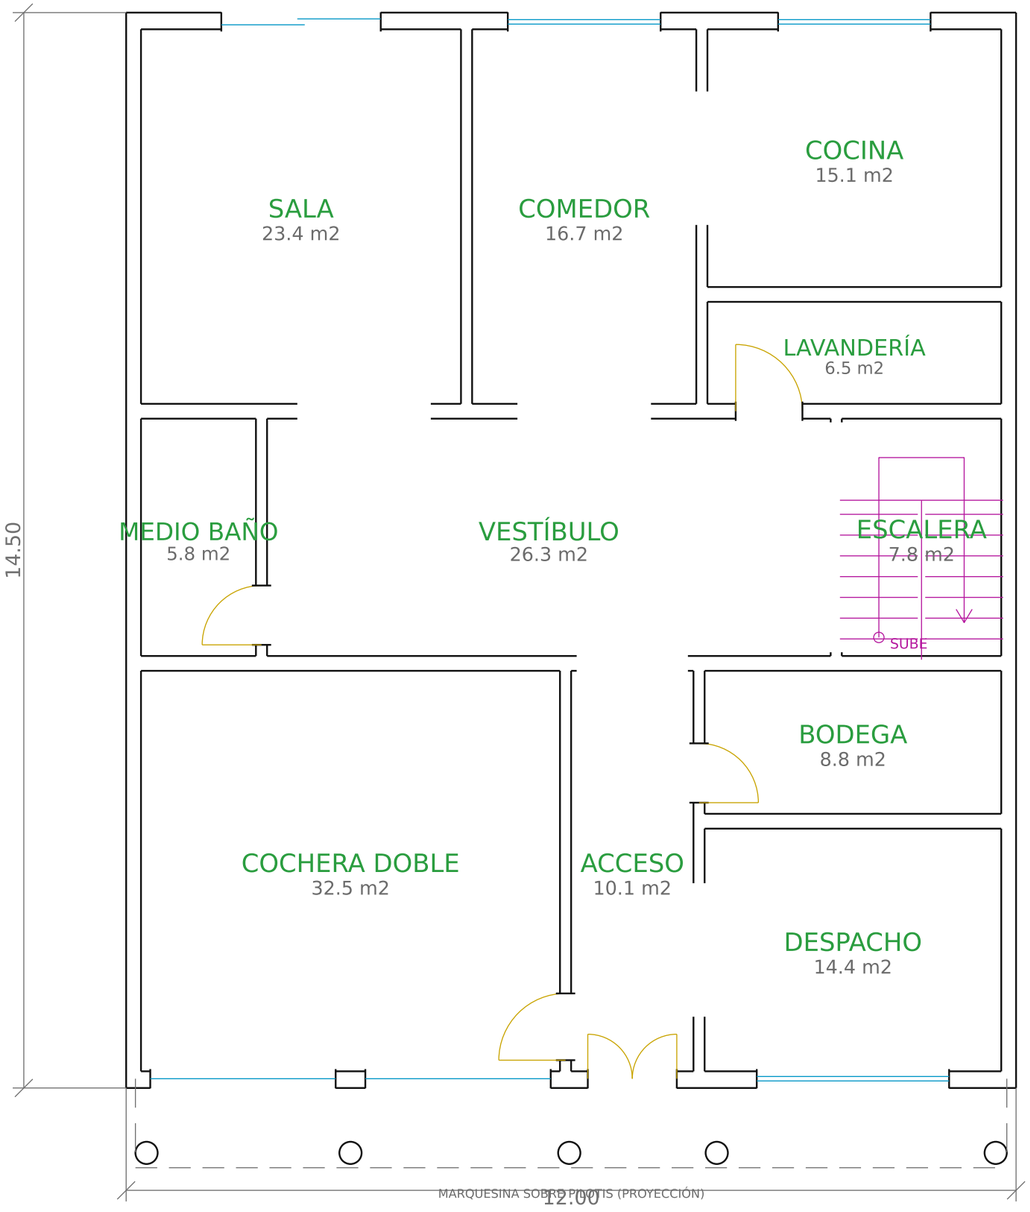

PLANTA BAJA — CASA

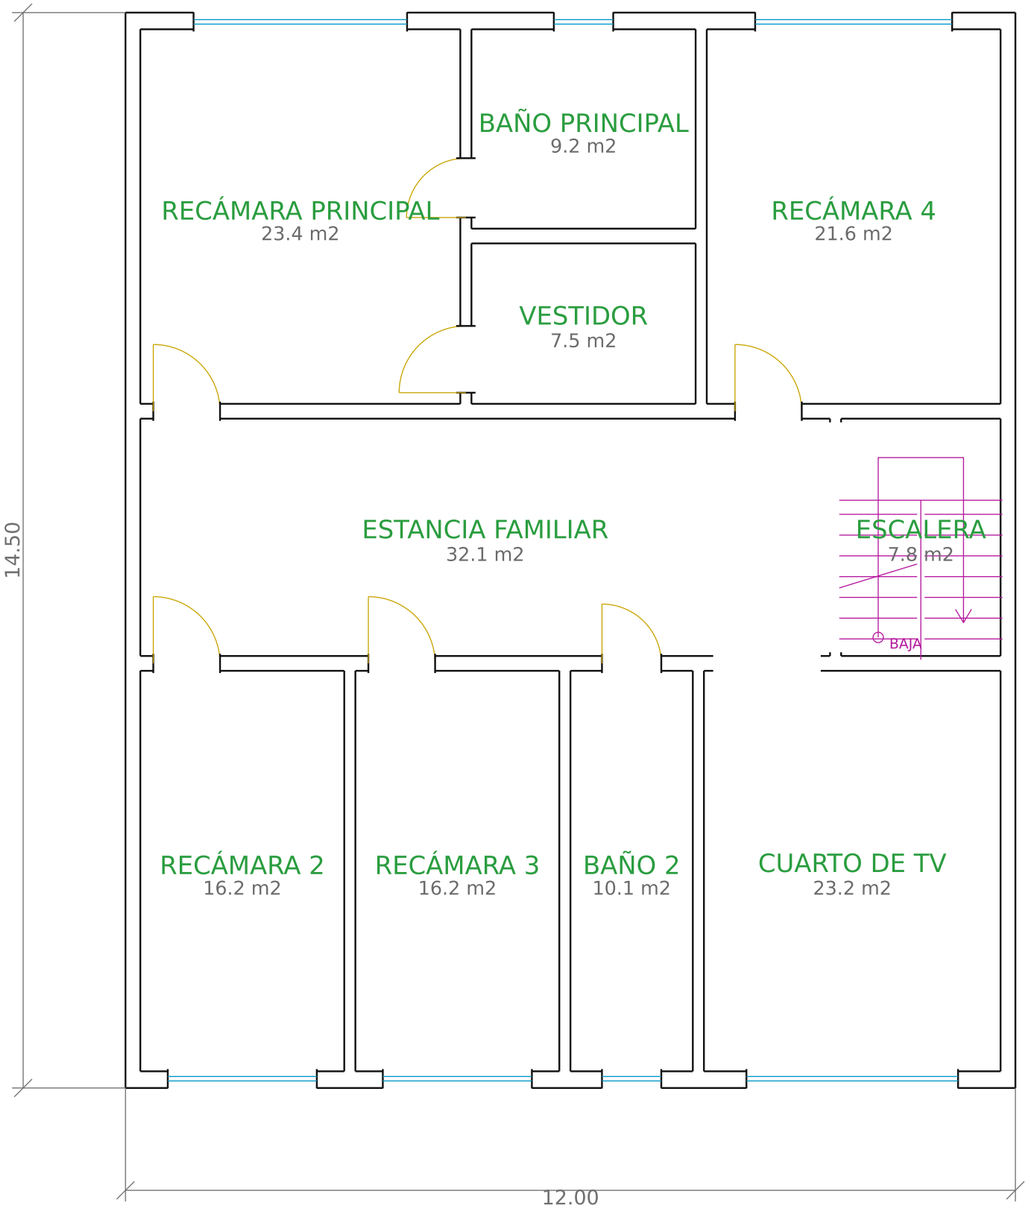

PLANTA ALTA — CASA

N

Cotas en metros. Verificar en sitio.
Anteproyecto: el proyecto ejecutivo (estructura, instalaciones, presupuesto y programa) se entrega por separado.
Normativa: Reglamento de Edificaciones de Tijuana y NTC-2017.

VÉRTICE Ingeniería, Arquitectura y Proyectos

CASA PILOTIS

AP-02 Plantas arquitectónicas

Clave: 2026-11-07-casa-moderna-bauhaus Fecha: 2026-11-07 Unidades: metros
Anteproyecto generado automáticamente — sin validez para construcción
Para revisión de: Ing. Miguel Estrada (DRO / Perito en edificación)

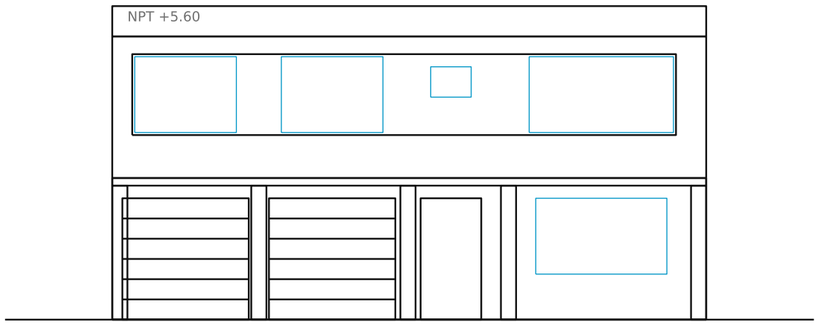

FACHADA PRINCIPAL (SUR)

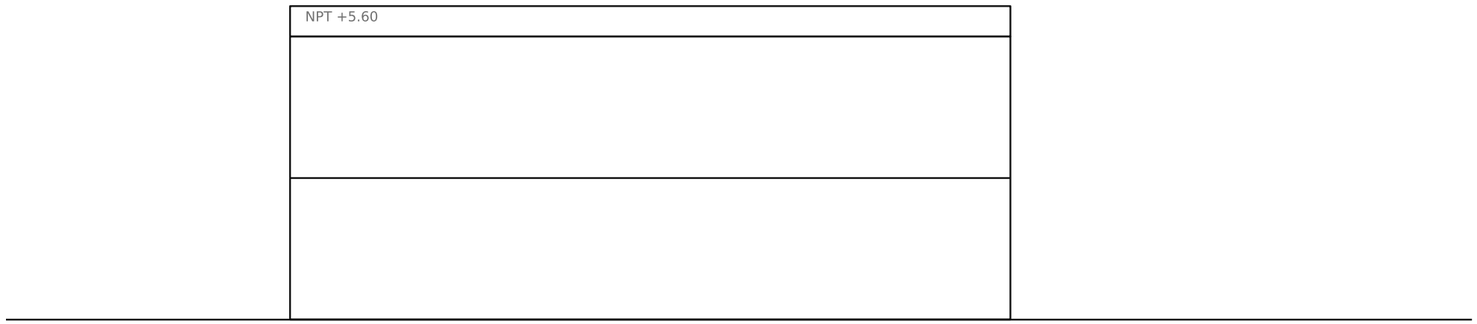

FACHADA LATERAL (ORIENTE)

CORTE LONGITUDINAL A-A'

N

Cotas en metros. Verificar en sitio.
Anteproyecto: el proyecto ejecutivo (estructura, instalaciones, presupuesto y programa) se entrega por separado.
Normativa: Reglamento de Edificaciones de Tijuana y NTC-2017.

VÉRTICE Ingeniería, Arquitectura y Proyectos

CASA PILOTIS

AP-03 Fachadas y corte

Clave: 2026-11-07-casa-moderna-bauhaus Fecha: 2026-11-07 Unidades: metros
Anteproyecto generado automáticamente — sin validez para construcción
Para revisión de: Ing. Miguel Estrada (DRO / Perito en edificación)