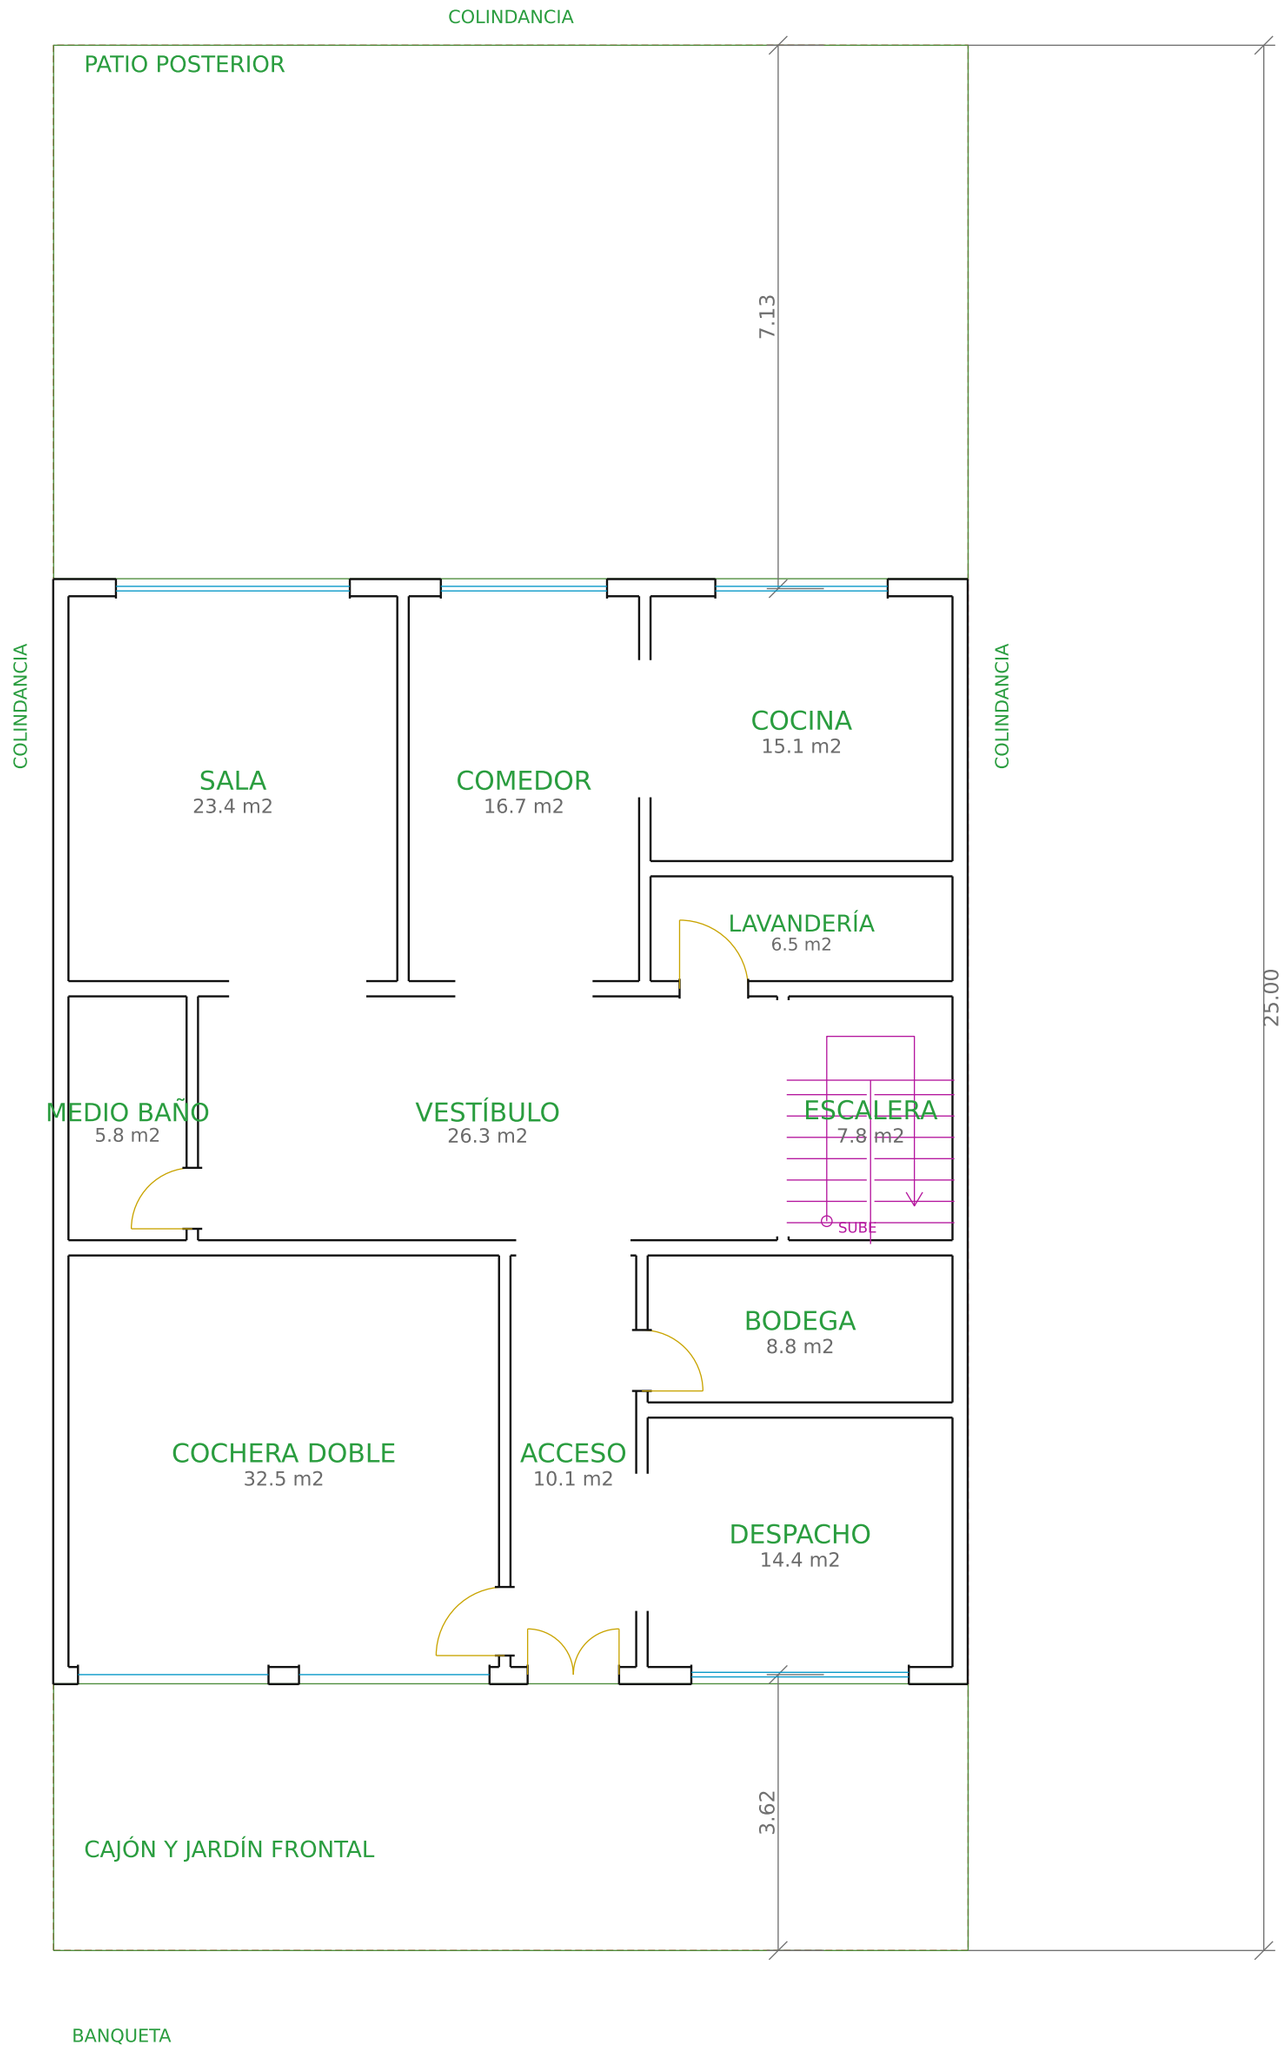


## CUADRO DE ÁREAS

| | |
|---|---|
| Terreno | 300.00 m2 |
| Desplante | 167.44 m2 |
| C.O.S. | 0.56 |
| Construcción total | 334.88 m2 |
| C.U.S. | 1.12 |
| Área libre | 132.56 m2 |
| Área verde (aprox.) | 84.00 m2 |
| Niveles | 2 |
| Cajones de estacionamiento | 2 |

N

Cotas en metros. Verificar en sitio.
Anteproyecto: el proyecto ejecutivo (estructura, instalaciones, presupuesto y programa) se entrega por separado.
Normativa: Reglamento de Edificaciones de Tijuana y NTC-2017.

VÉRTICE Ingeniería, Arquitectura y Proyectos

CASA FRACTURA

AP-01 Planta de conjunto

Clave: 2026-11-03-casa-deconstructivista Fecha: 2026-11-03 Unidades: metros
Anteproyecto generado automáticamente — sin validez para construcción
Para revisión de: Ing. Miguel Estrada (DRO / Perito en edificación)

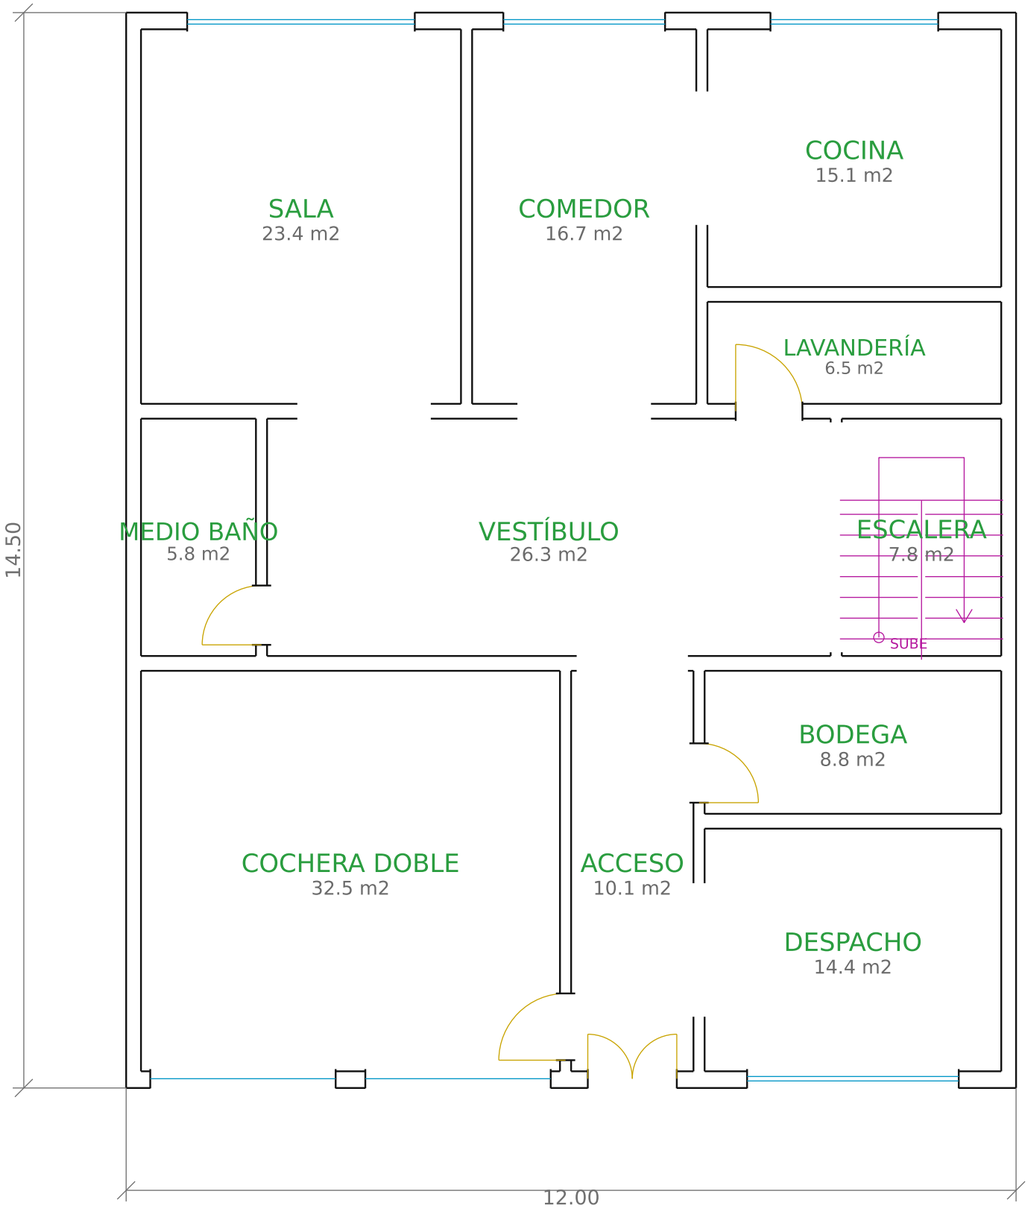


PLANTA BAJA — CASA

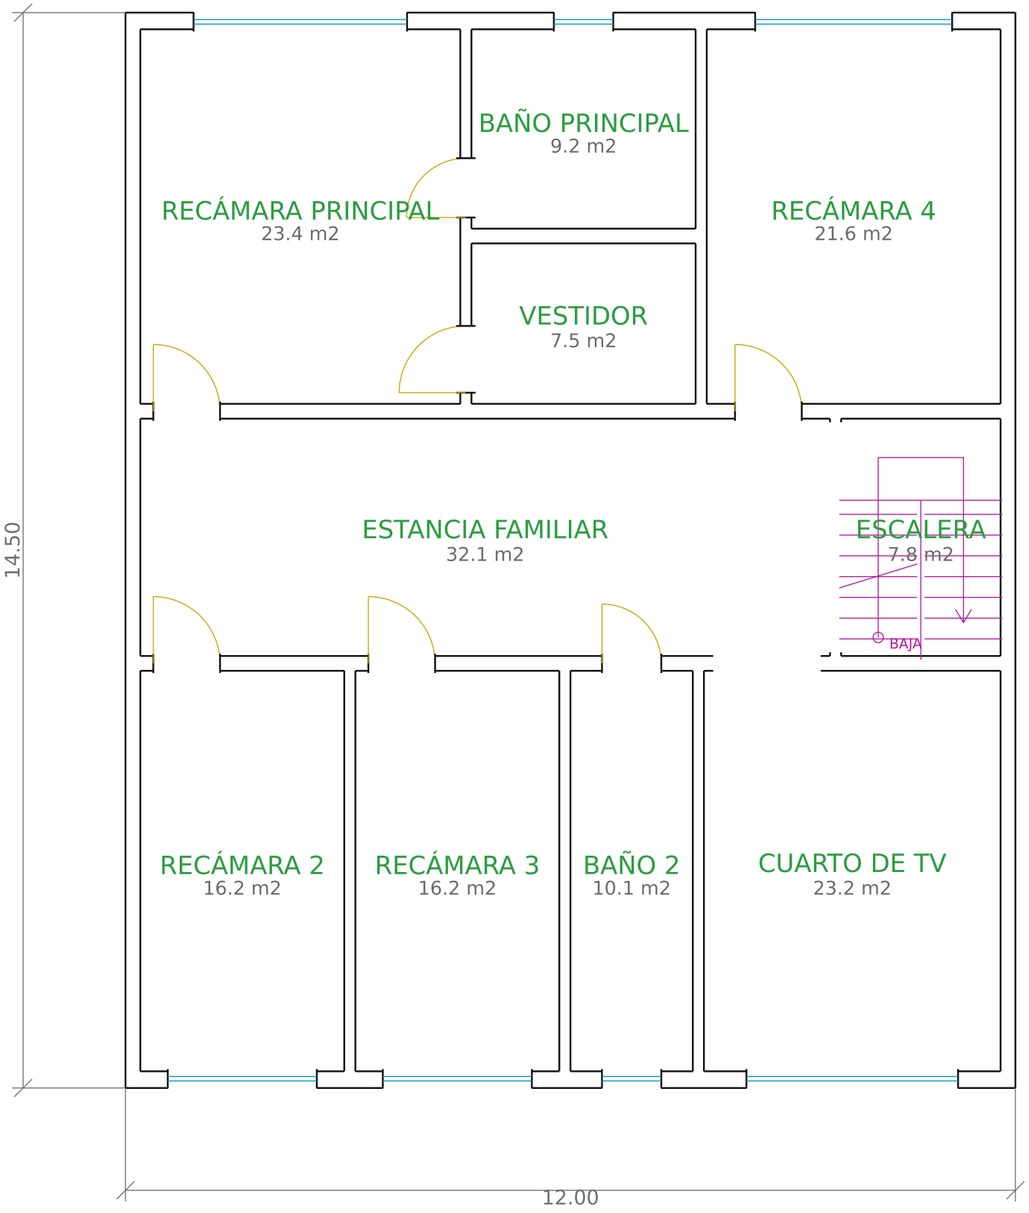


PLANTA ALTA — CASA

N

Cotas en metros. Verificar en sitio.
Anteproyecto: el proyecto ejecutivo (estructura, instalaciones, presupuesto y programa) se entrega por separado.
Normativa: Reglamento de Edificaciones de Tijuana y NTC-2017.

VÉRTICE Ingeniería, Arquitectura y Proyectos

CASA FRACTURA

AP-02 Plantas arquitectónicas

Clave: 2026-11-03-casa-deconstructivista Fecha: 2026-11-03 Unidades: metros
Anteproyecto generado automáticamente — sin validez para construcción
Para revisión de: Ing. Miguel Estrada (DRO / Perito en edificación)

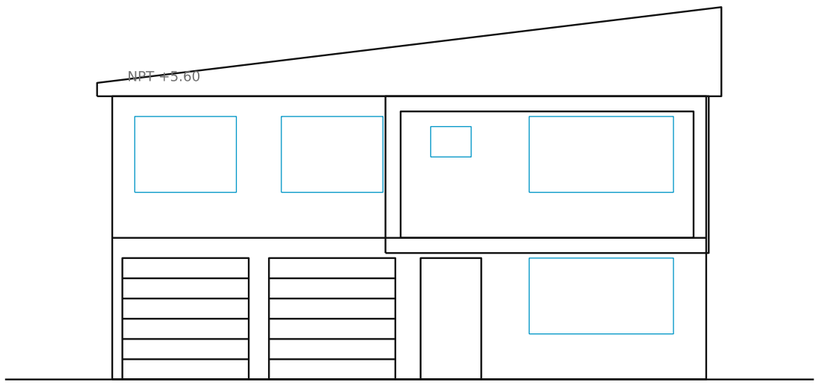


FACHADA PRINCIPAL (SUR)

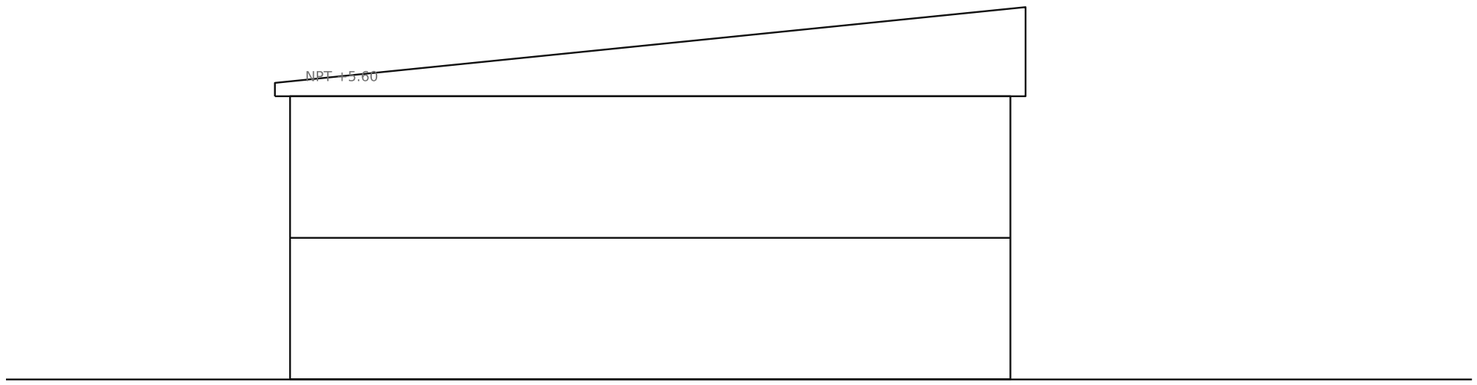


FACHADA LATERAL (ORIENTE)

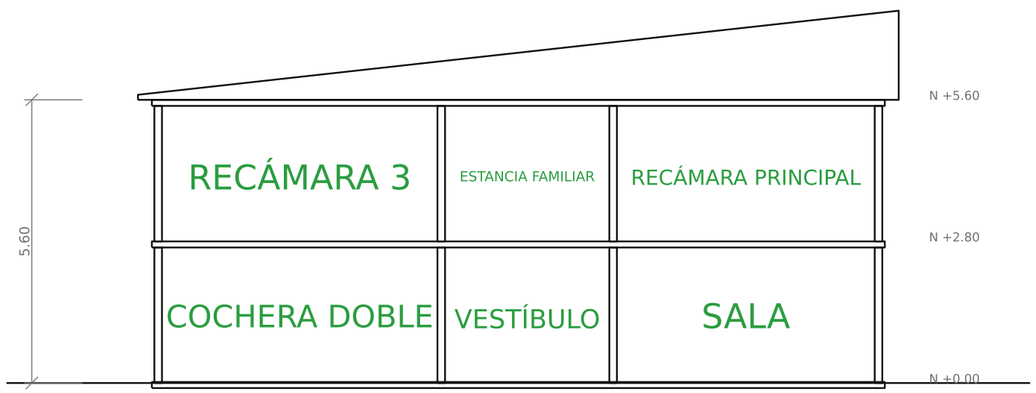


CORTE LONGITUDINAL A-A'

N

Cotas en metros. Verificar en sitio.
Anteproyecto: el proyecto ejecutivo (estructura, instalaciones, presupuesto y programa) se entrega por separado.
Normativa: Reglamento de Edificaciones de Tijuana y NTC-2017.

VÉRTICE Ingeniería, Arquitectura y Proyectos

CASA FRACTURA

AP-03 Fachadas y corte

Clave: 2026-11-03-casa-deconstructivista Fecha: 2026-11-03 Unidades: metros
Anteproyecto generado automáticamente — sin validez para construcción
Para revisión de: Ing. Miguel Estrada (DRO / Perito en edificación)